

PERMIS DE CONSTRUIRE
CONSTRUCTION D'UNE MAISON INDIVIDUELLE




ADRESSE DU PROJET

BENEFICIAIRE:

MAITRE D'OUVRAGE:


PLAN DU DOSSIER

PCMI1 Plan de situation
PCMI2 Plan de masse initial et projeté
PCMI3 Plan de coupe projeté
PCMI4 Notice descriptive
PCMI5 Plan des façades et de toiture
PCMI6 Insertion graphique
PCMI7 Photographie proche
PCMI8 Photographie lointaine
Annexes

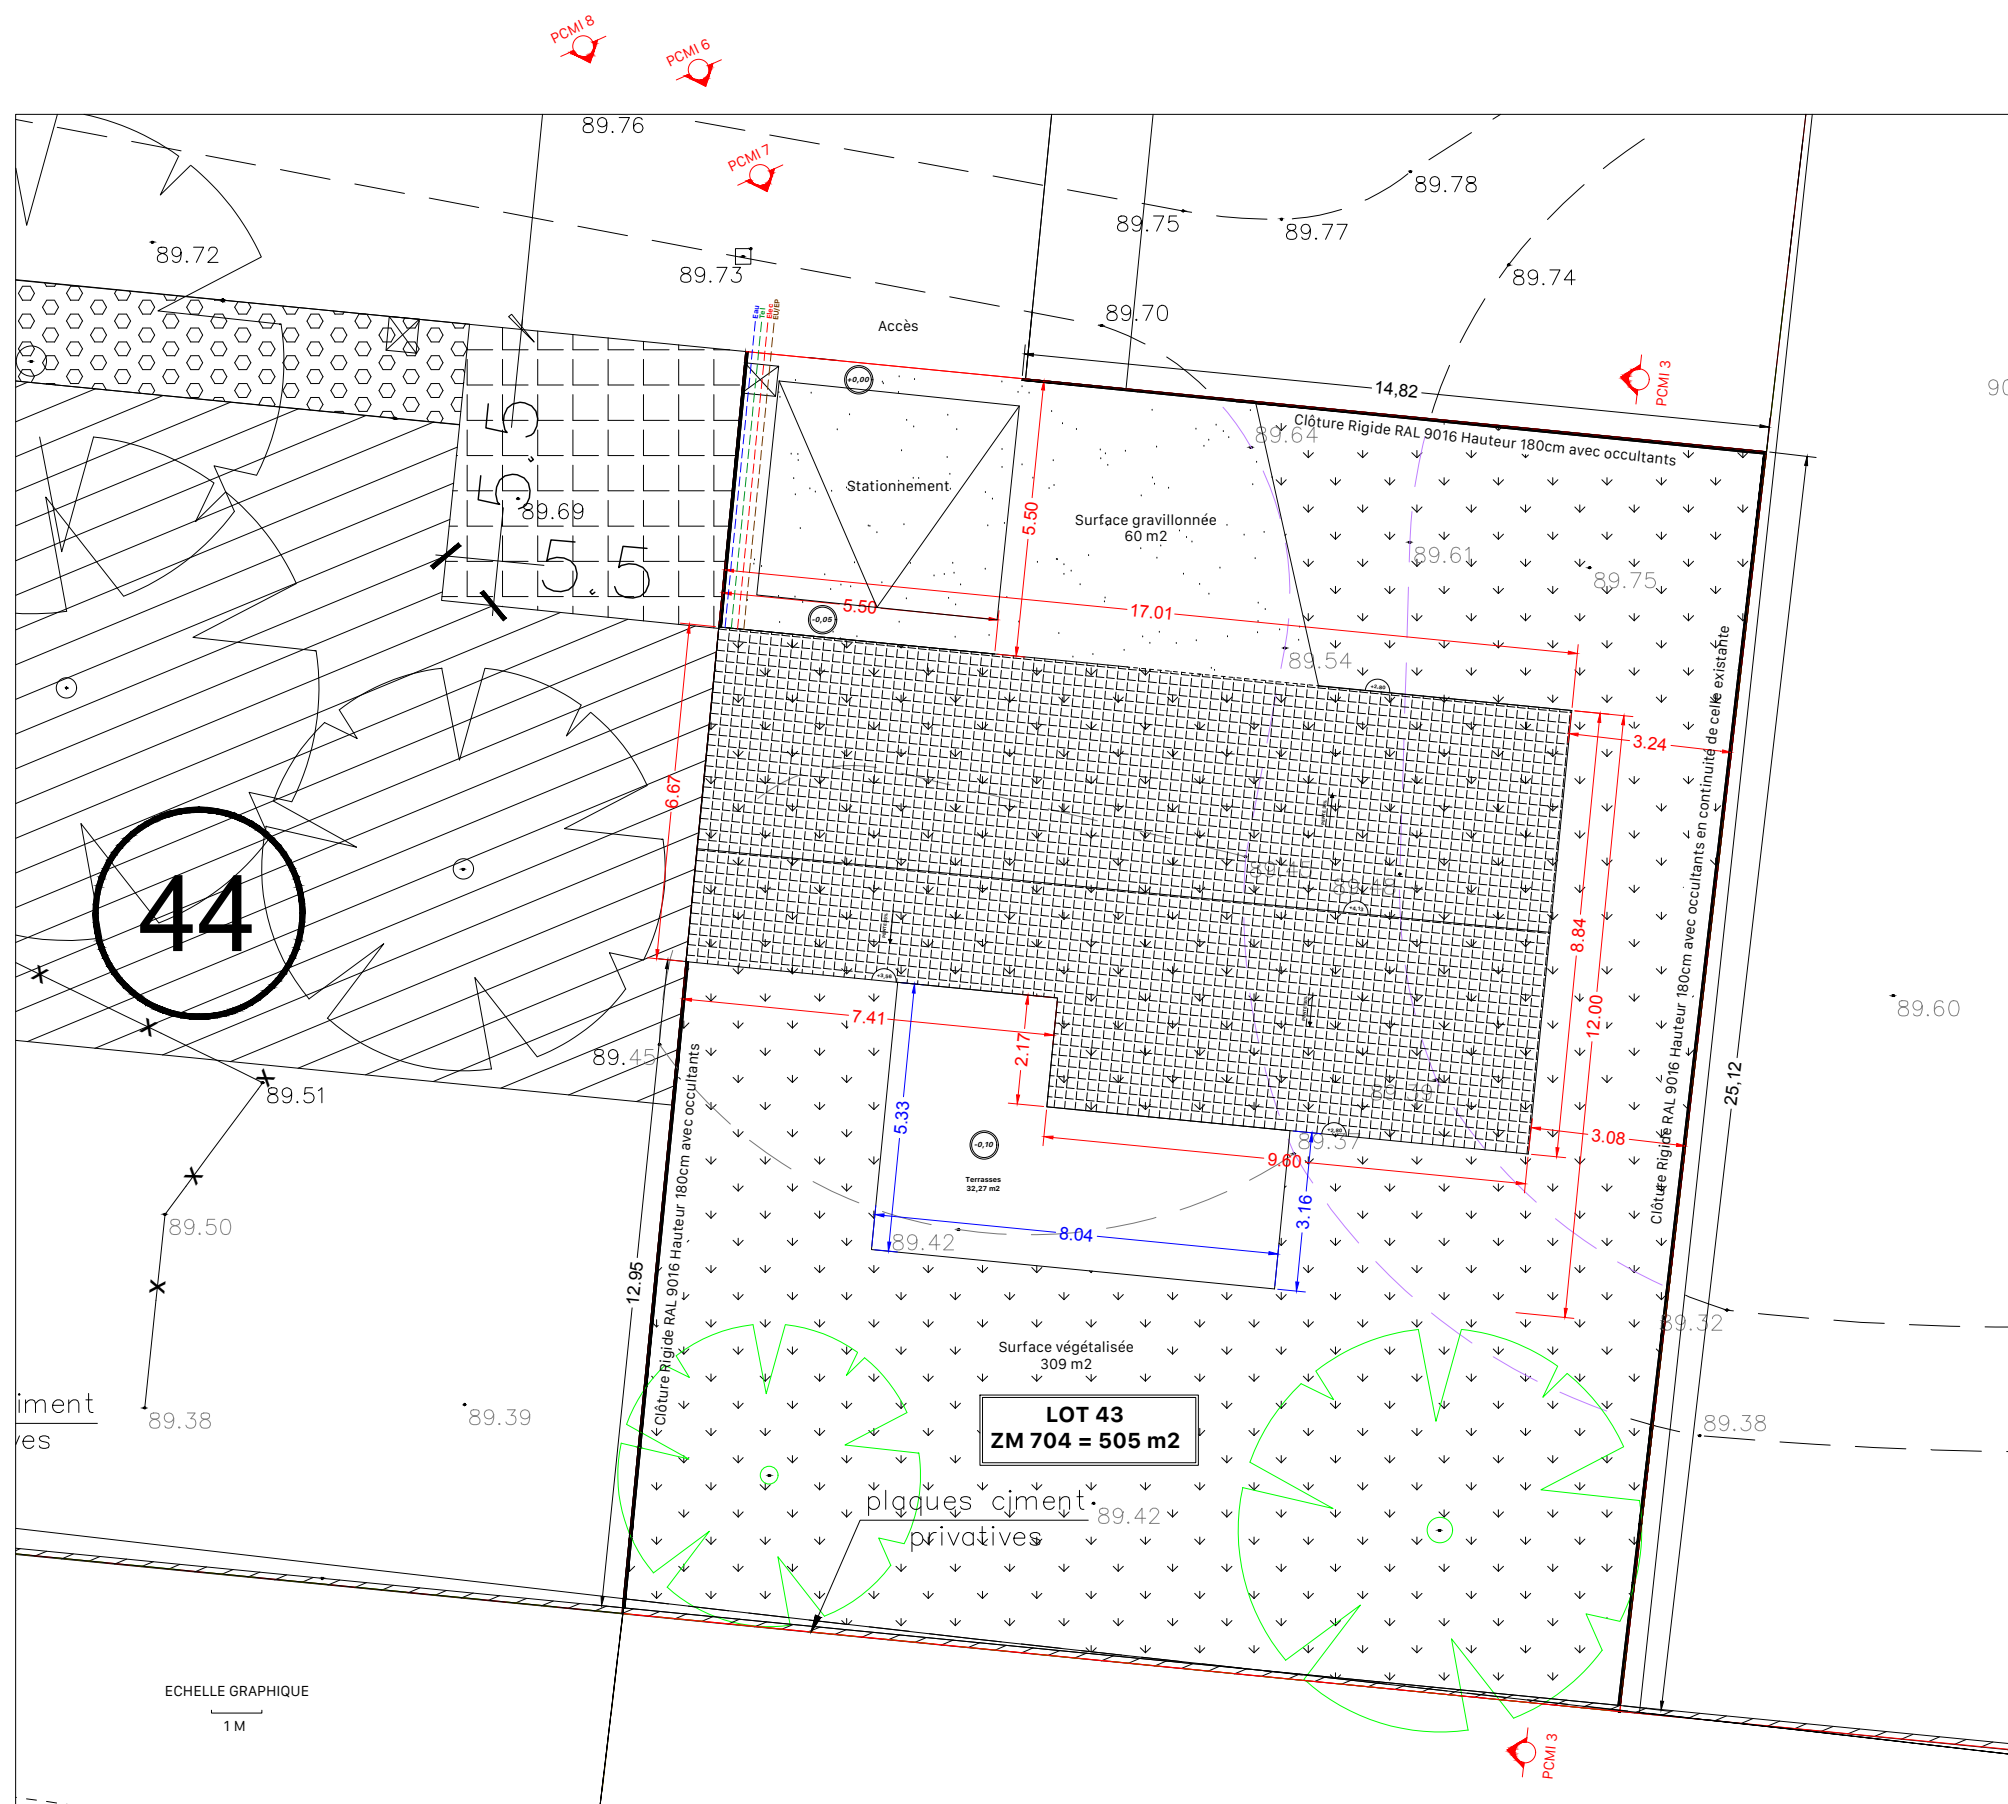

PCMI 2 - Plan de masse Projeté

Ech 1/150 (Format A3)

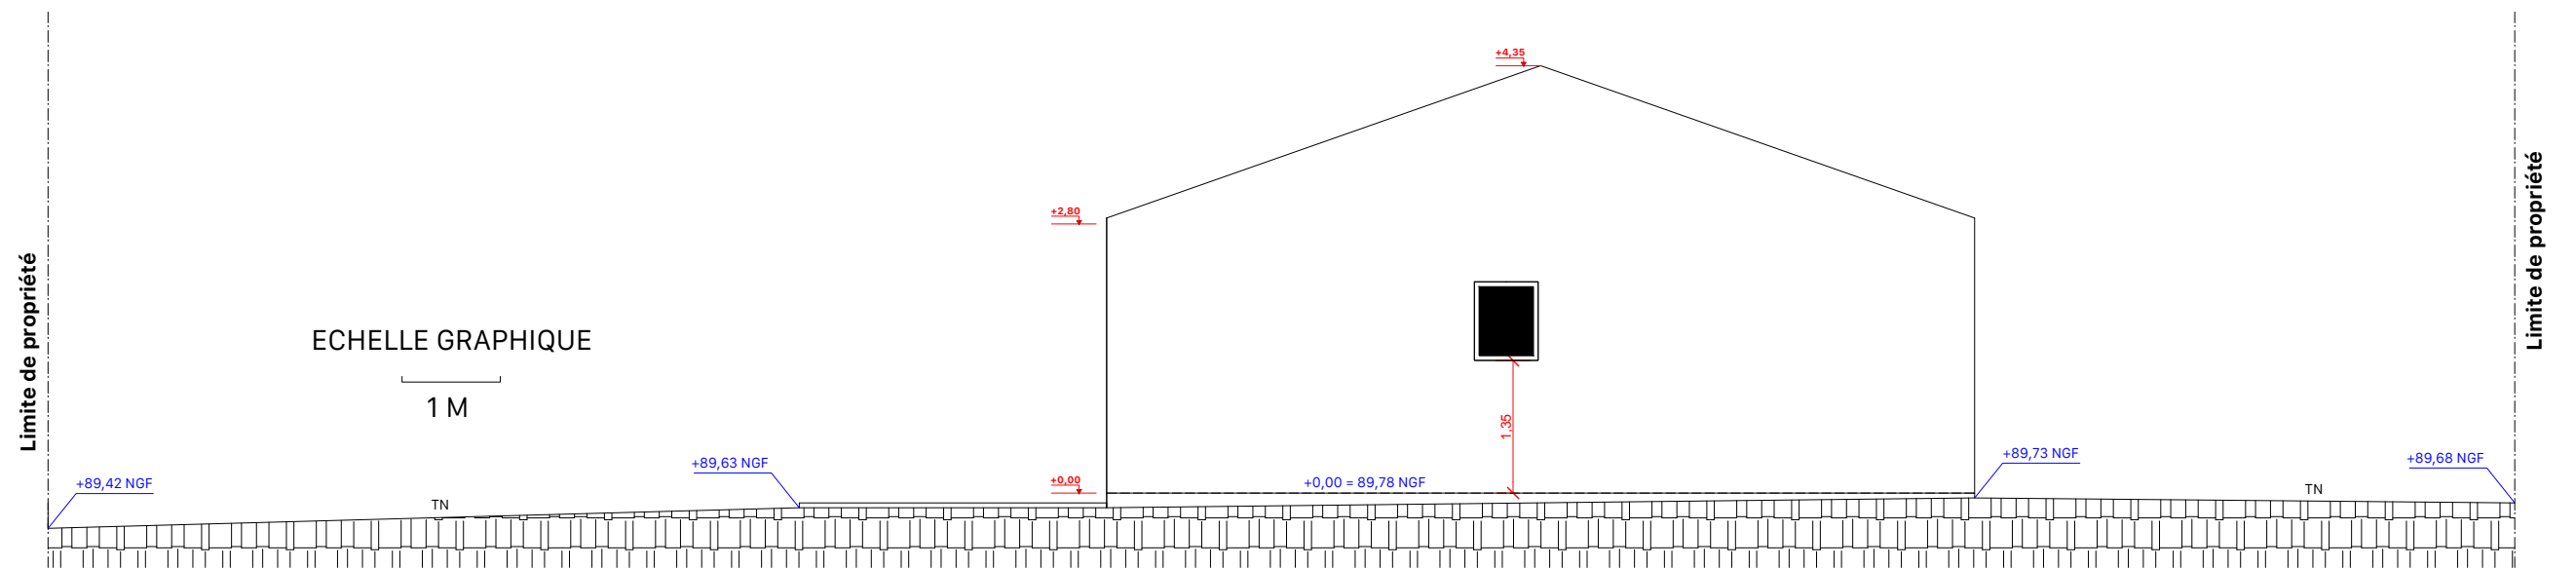

PCMI 3 - Coupe longitudinale du terrain
Ech 1/75 (Format A3)

1. L'ENVIRONNEMENT DU TERRAIN

Localisation

2. LE PROJET

Aménagements

Les travaux à réaliser consistent à construire une nouvelle maison d'habitation de style moderne à 1 niveau. Conservé le garage existant et démonter l'abris à poule (en taules) présent au milieu du terrain. Un muret de 120 cm avec un claustra alu sera réalisé autour des parcelles.

Aspect technique

Gros-oeuvre: Maçonnerie parpaing épaisseur 20cm
Enduit: Enduit blanc cassé gratté référence 001 de chez WEBER
Menuiseries extérieures en Aluminium Blanc 9016
Portail de garage Aluminium ral 9016 blanc
Couverture tuile en terre cuite demi ronde à dominance Rouge pour la partie habitation et garage
Gouttière aluminium ton blanc cassé au plus proche de l'enduit existant.
Empierrement sur la partie avant de la maison (accès garage et porte d'entrée)

Clôtures rigides RAL 7016 avec occultants autour de la parcelle (hors zone du fond déjà clôturée)

Accès au réseau

Accès:

Réseaux:

Traitement végétal

Une surface végétalisée de 309 m² sera préservée au sol pour assurer l'infiltration des eaux de pluie et limiter le ruissèlement vers les parcelles voisines.
La haie en façade de terrain sera conservée


3. LES SURFACES

Récapitulatif des surfaces

Surface de la parcelle

Après réalisation des travaux :


Surface d'emprise au sol de toutes les constructions projetées (maison + terrasse) = 1166 m²
Surface végétalisée = 309 m²
Surface gravillonnée = 60 m²
Places de stationnement Extérieures : 02Ext.
Surface de plancher de la construction projetée = 93,59 m²

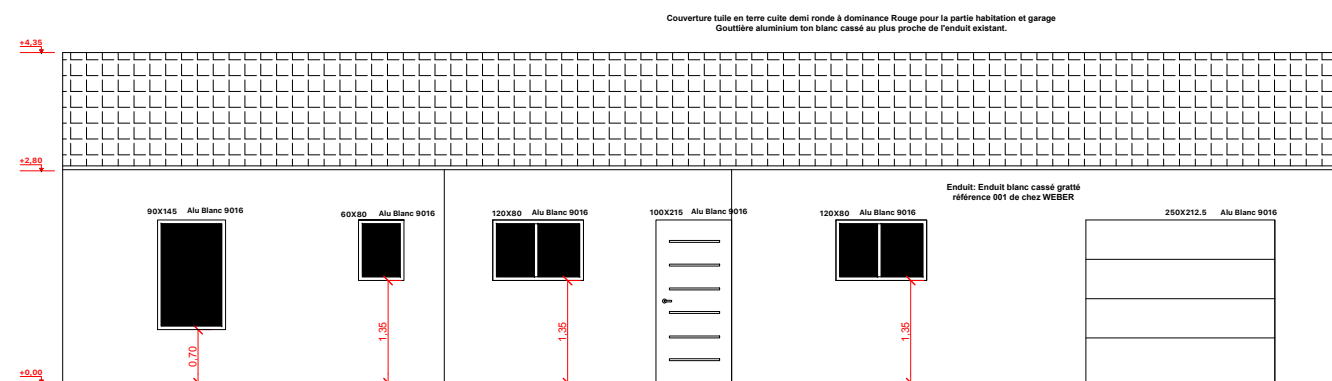


Façade Nord

ECHELLE GRAPHIQUE


1 M

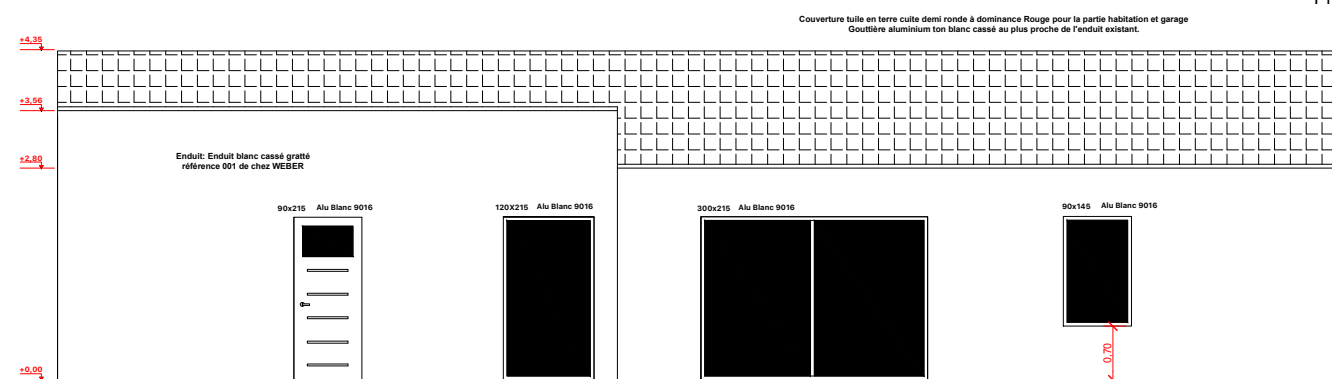

Façade Sud

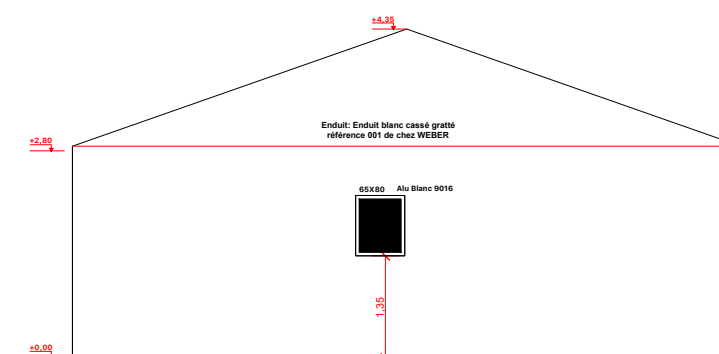


Façade Est

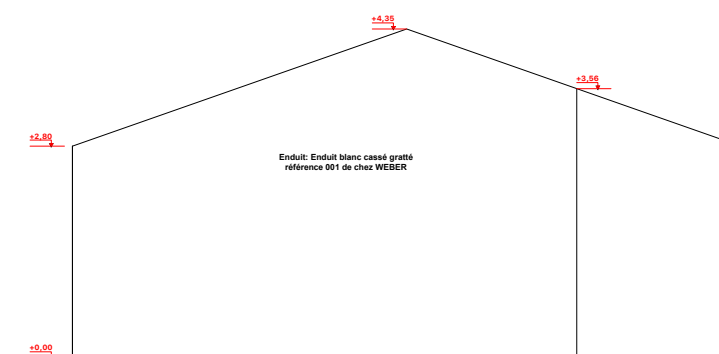

Façade Ouest

PCMI 5 - Plan des Façades projetées

Ech 1/100 (Format A3)

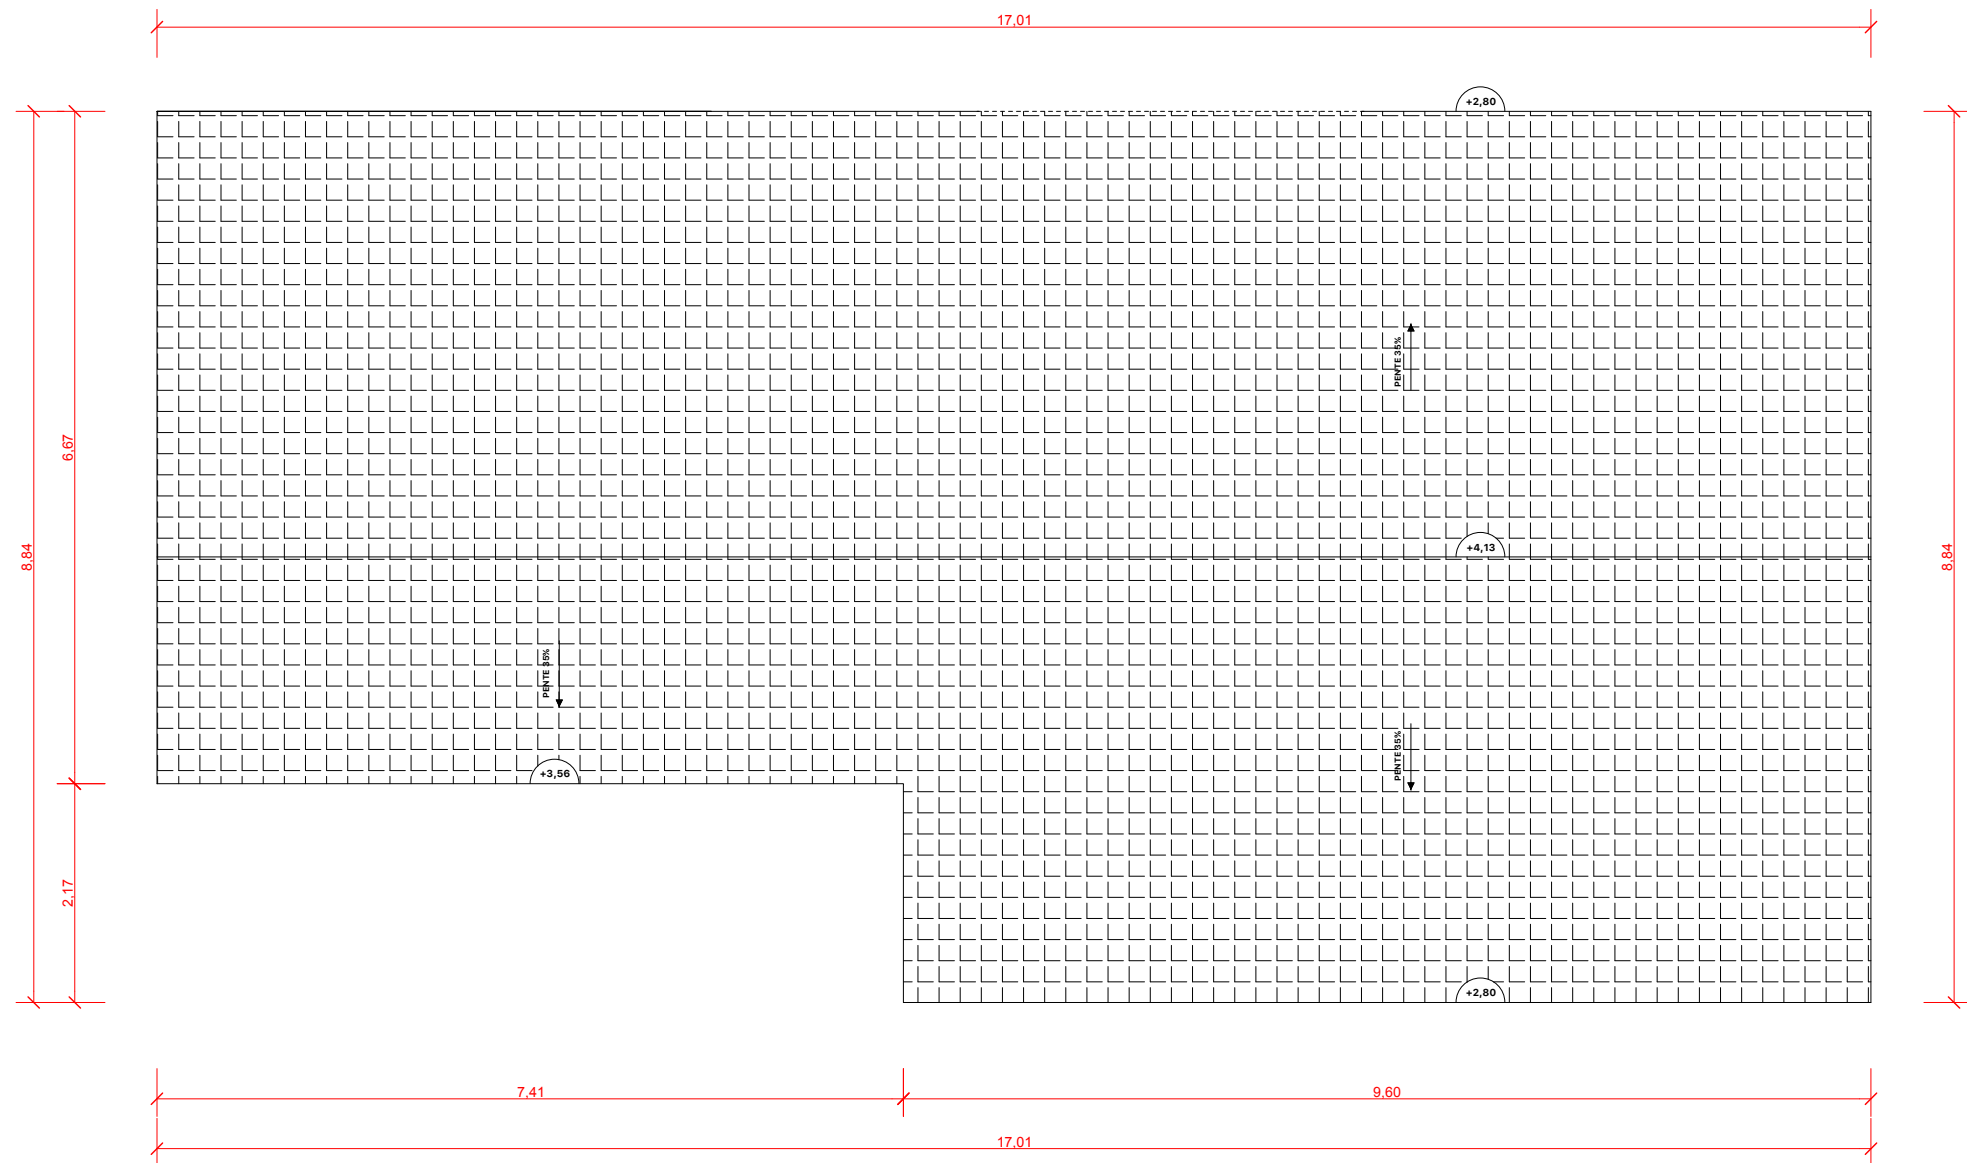

PCMI 5 - Plan des Toitures projetées
Ech 1/75(Format A3)



PCMI 6 - Insertion Graphique